



PROCESS FLOW DIAGRAM

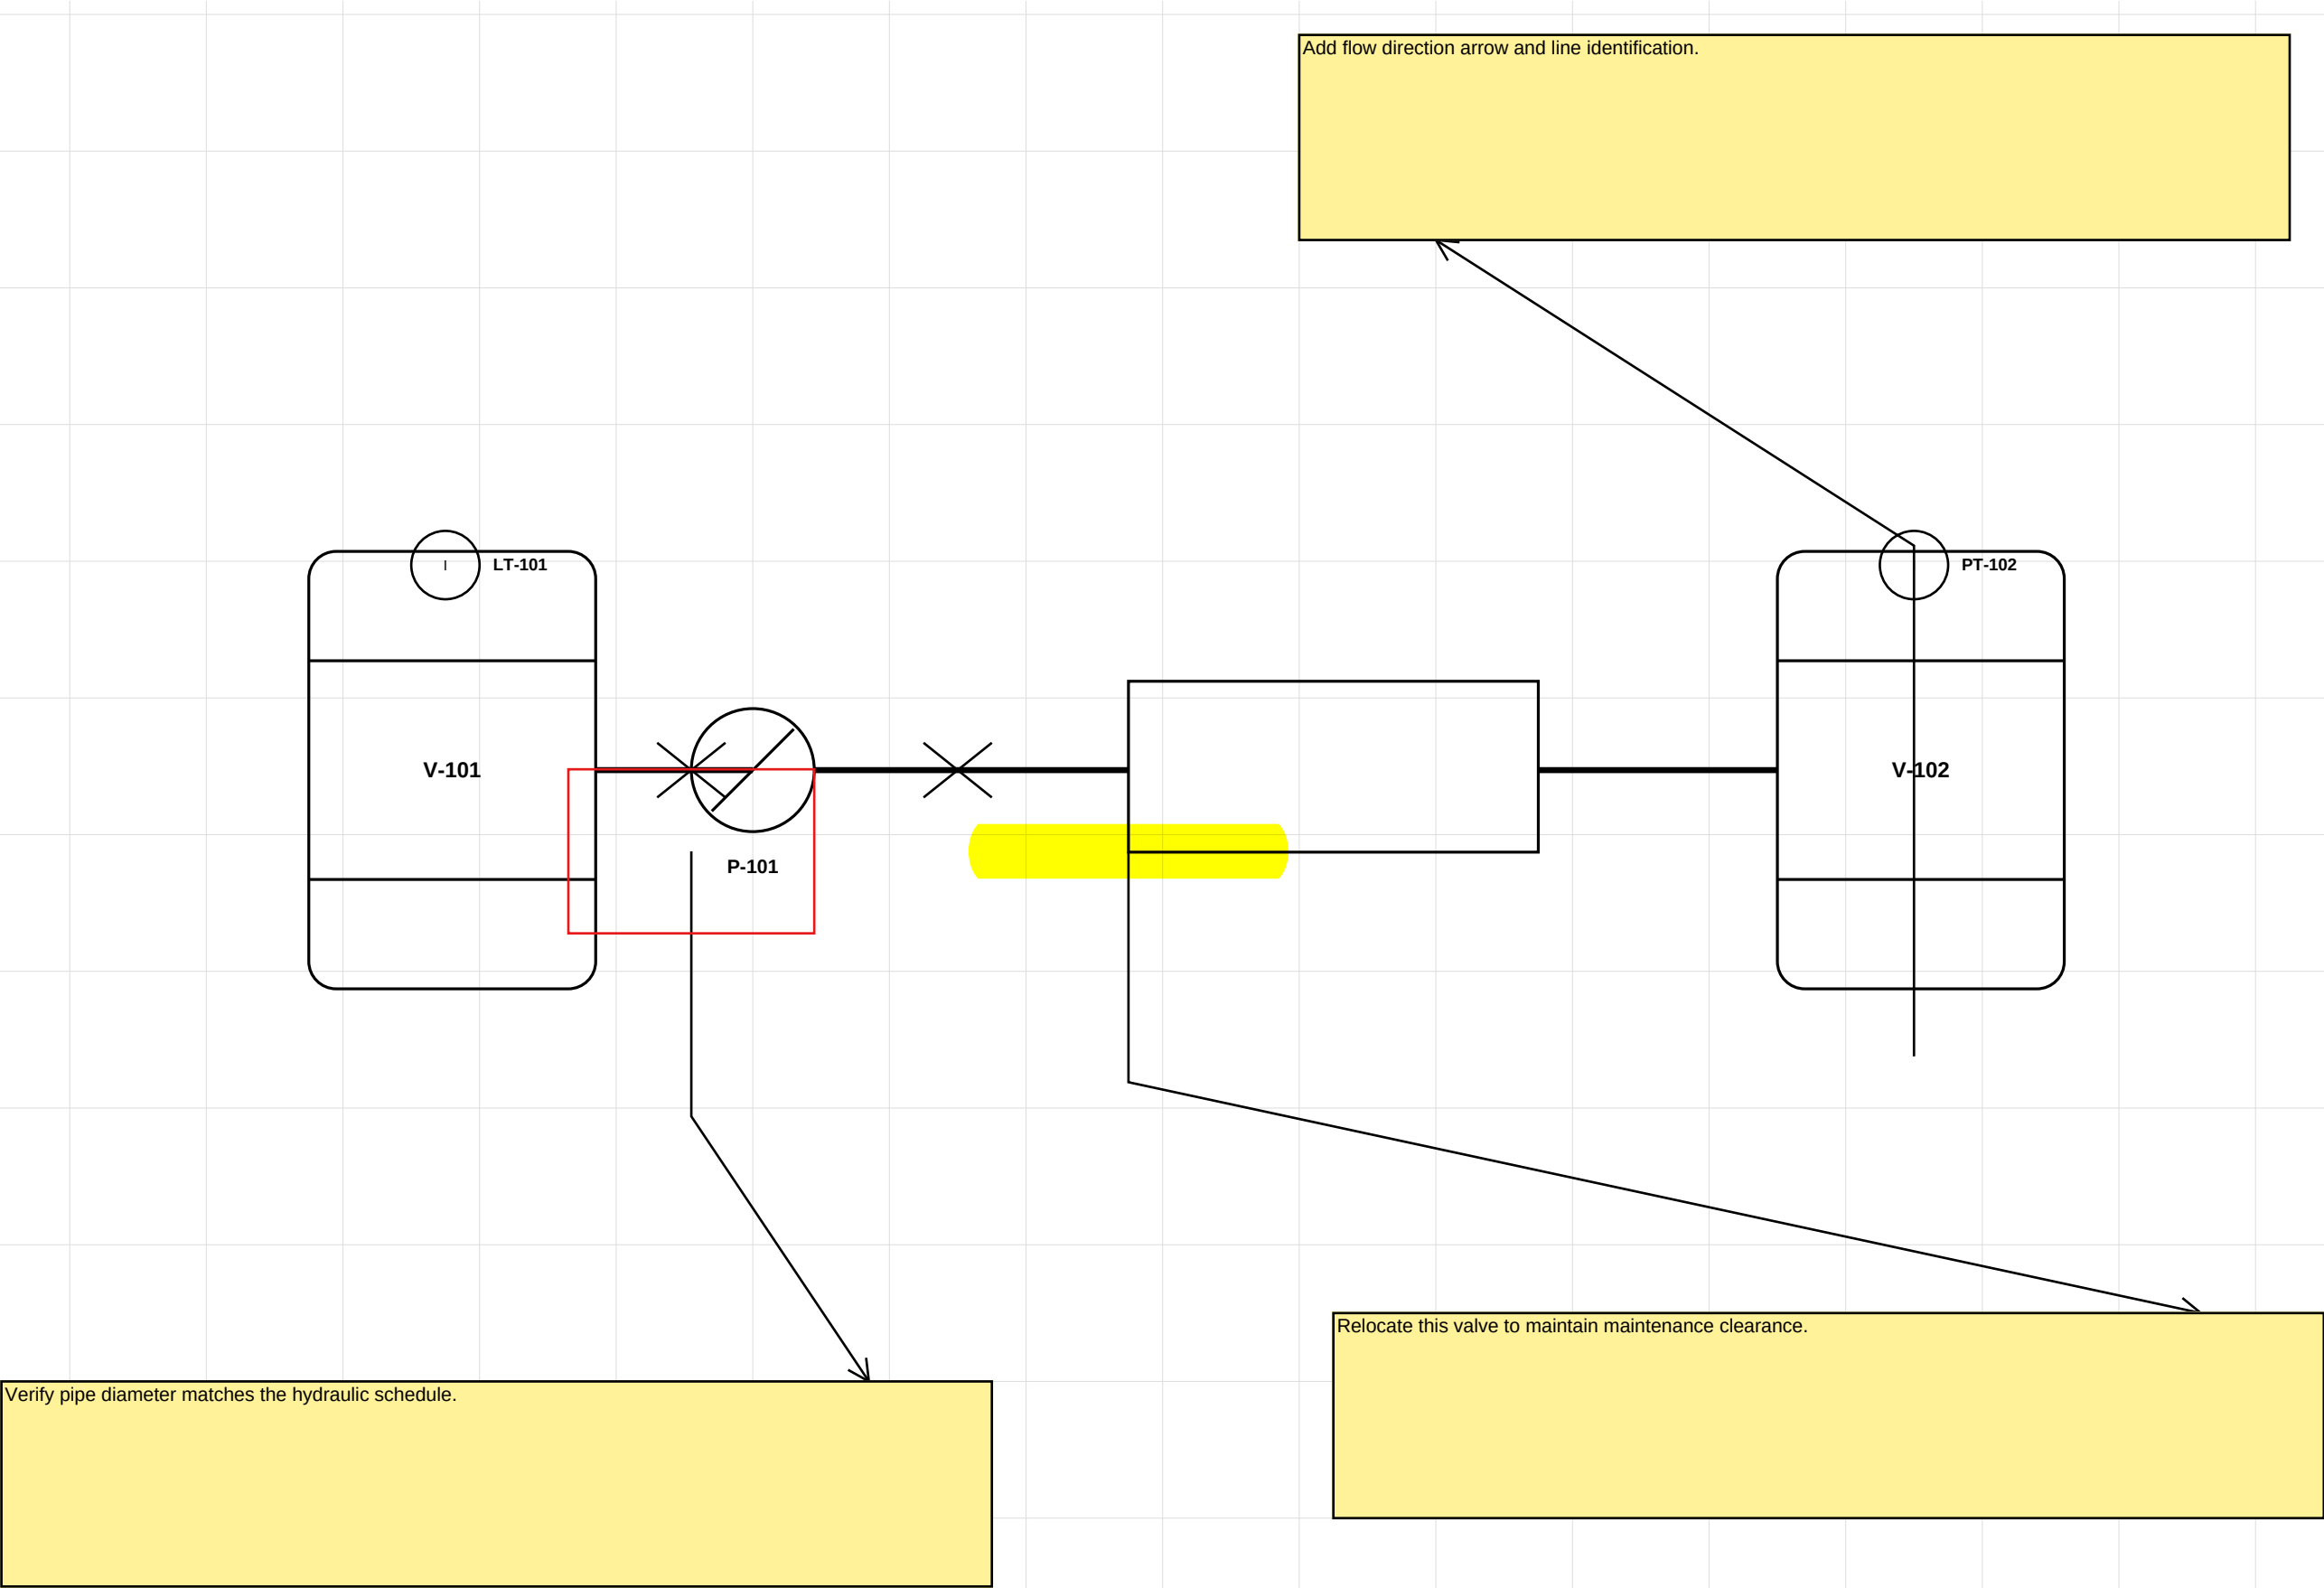

PIPING & INSTRUMENTATION LAYOUT

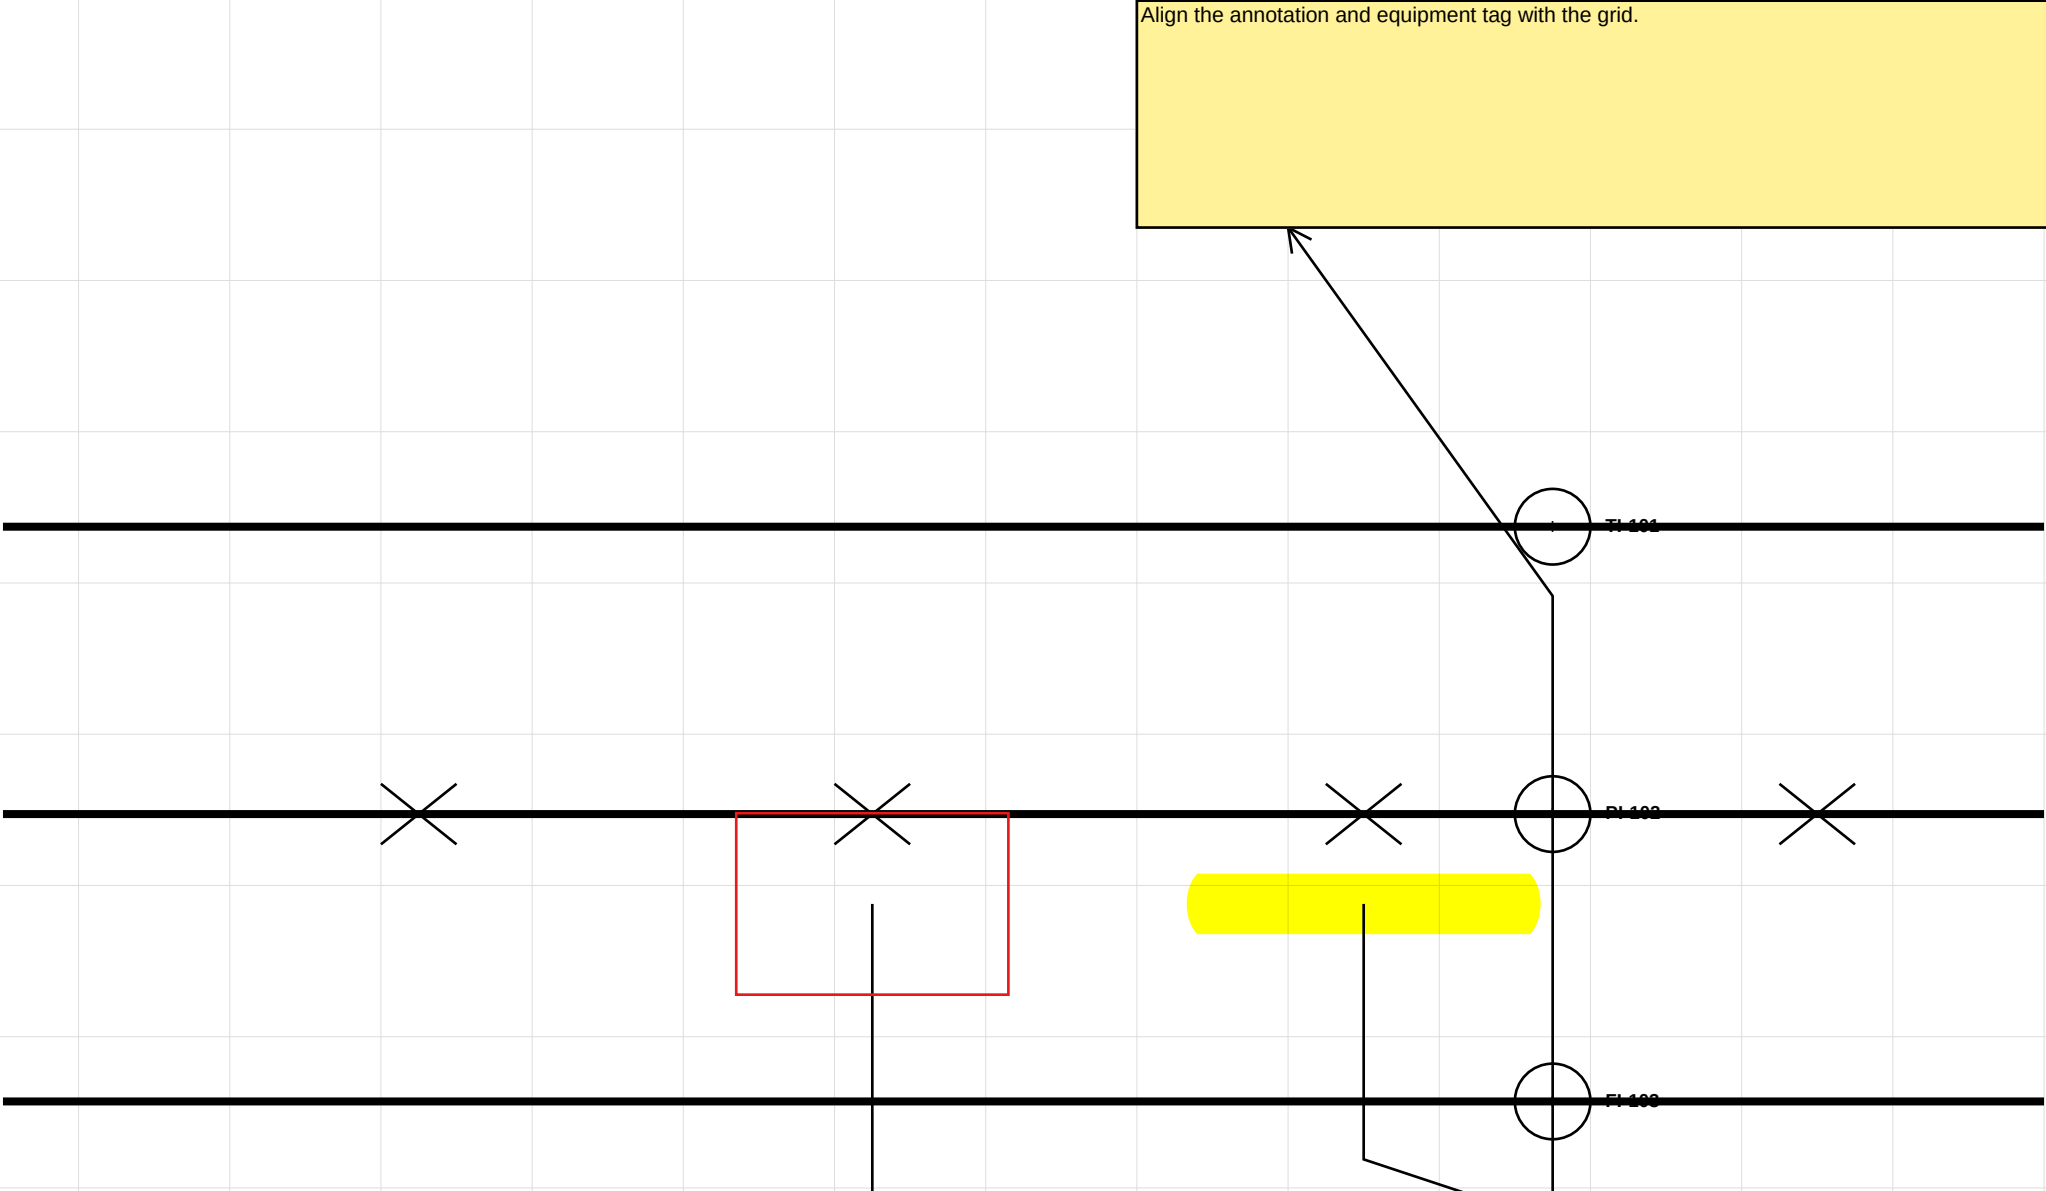


Align the annotation and equipment tag with the grid.


Confirm equipment nozzle orientation before issue.

Check this branch against the structural opening.


GENERAL PLANT LAYOUT

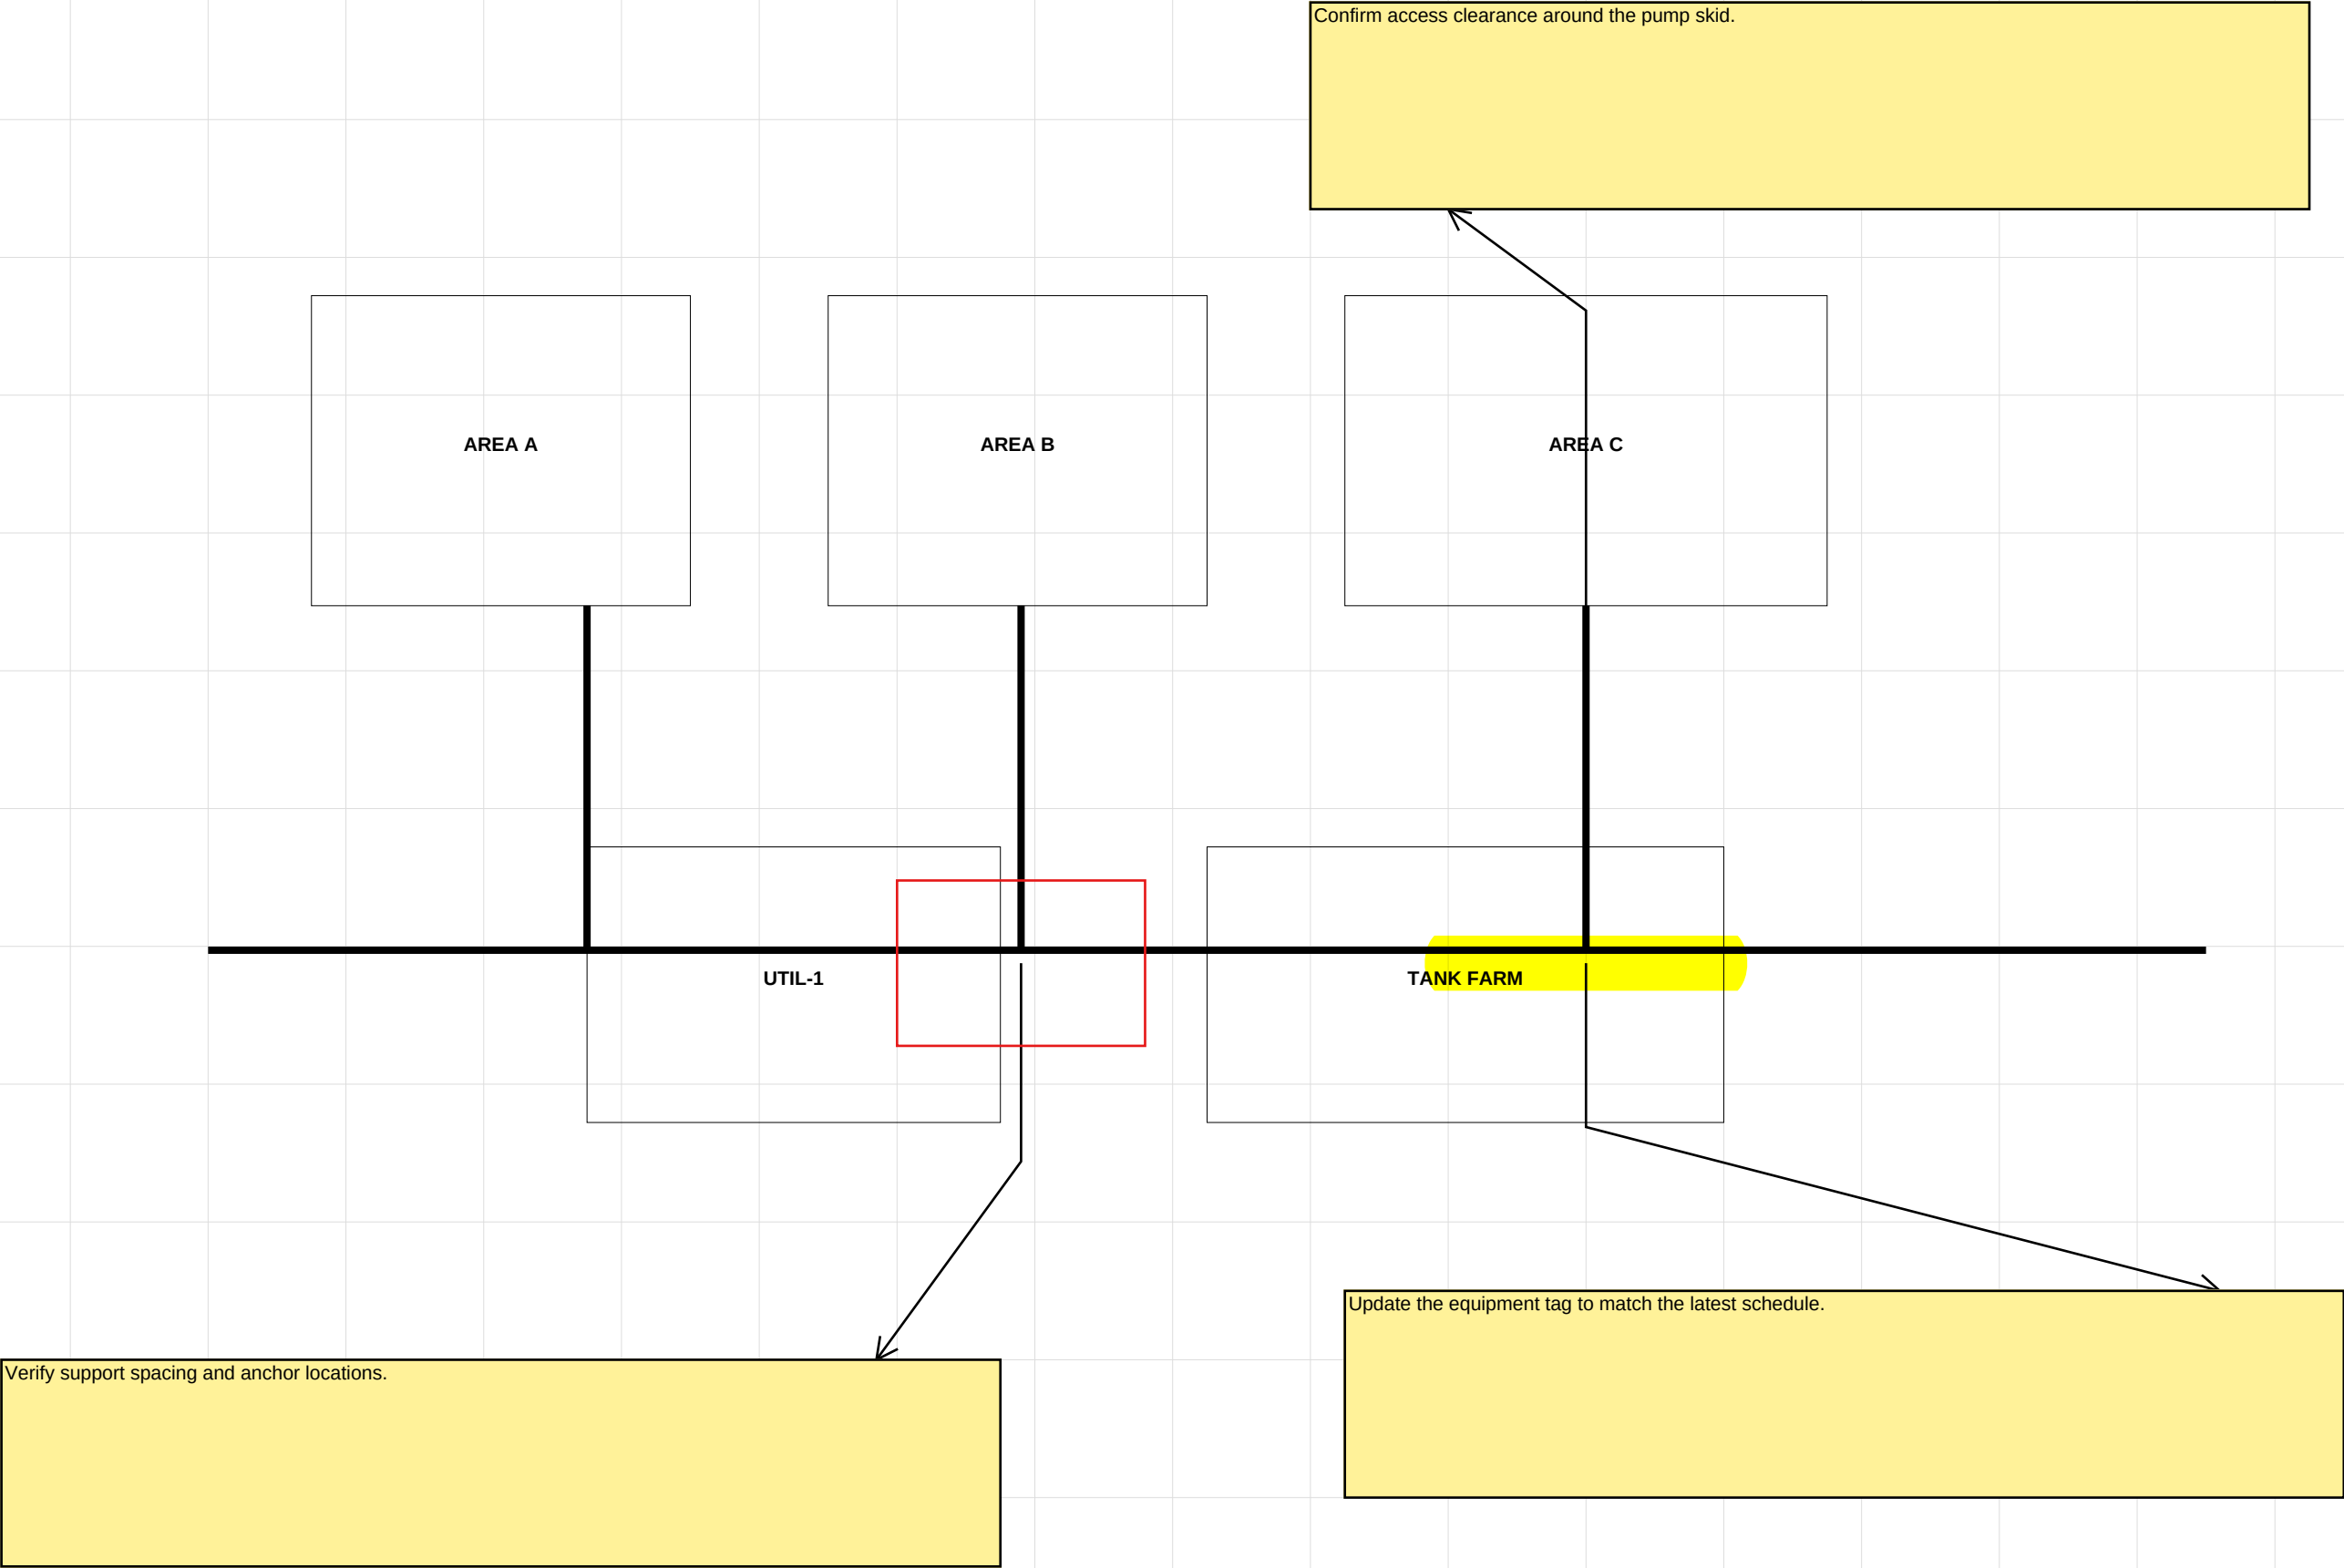


EQUIPMENT ARRANGEMENT

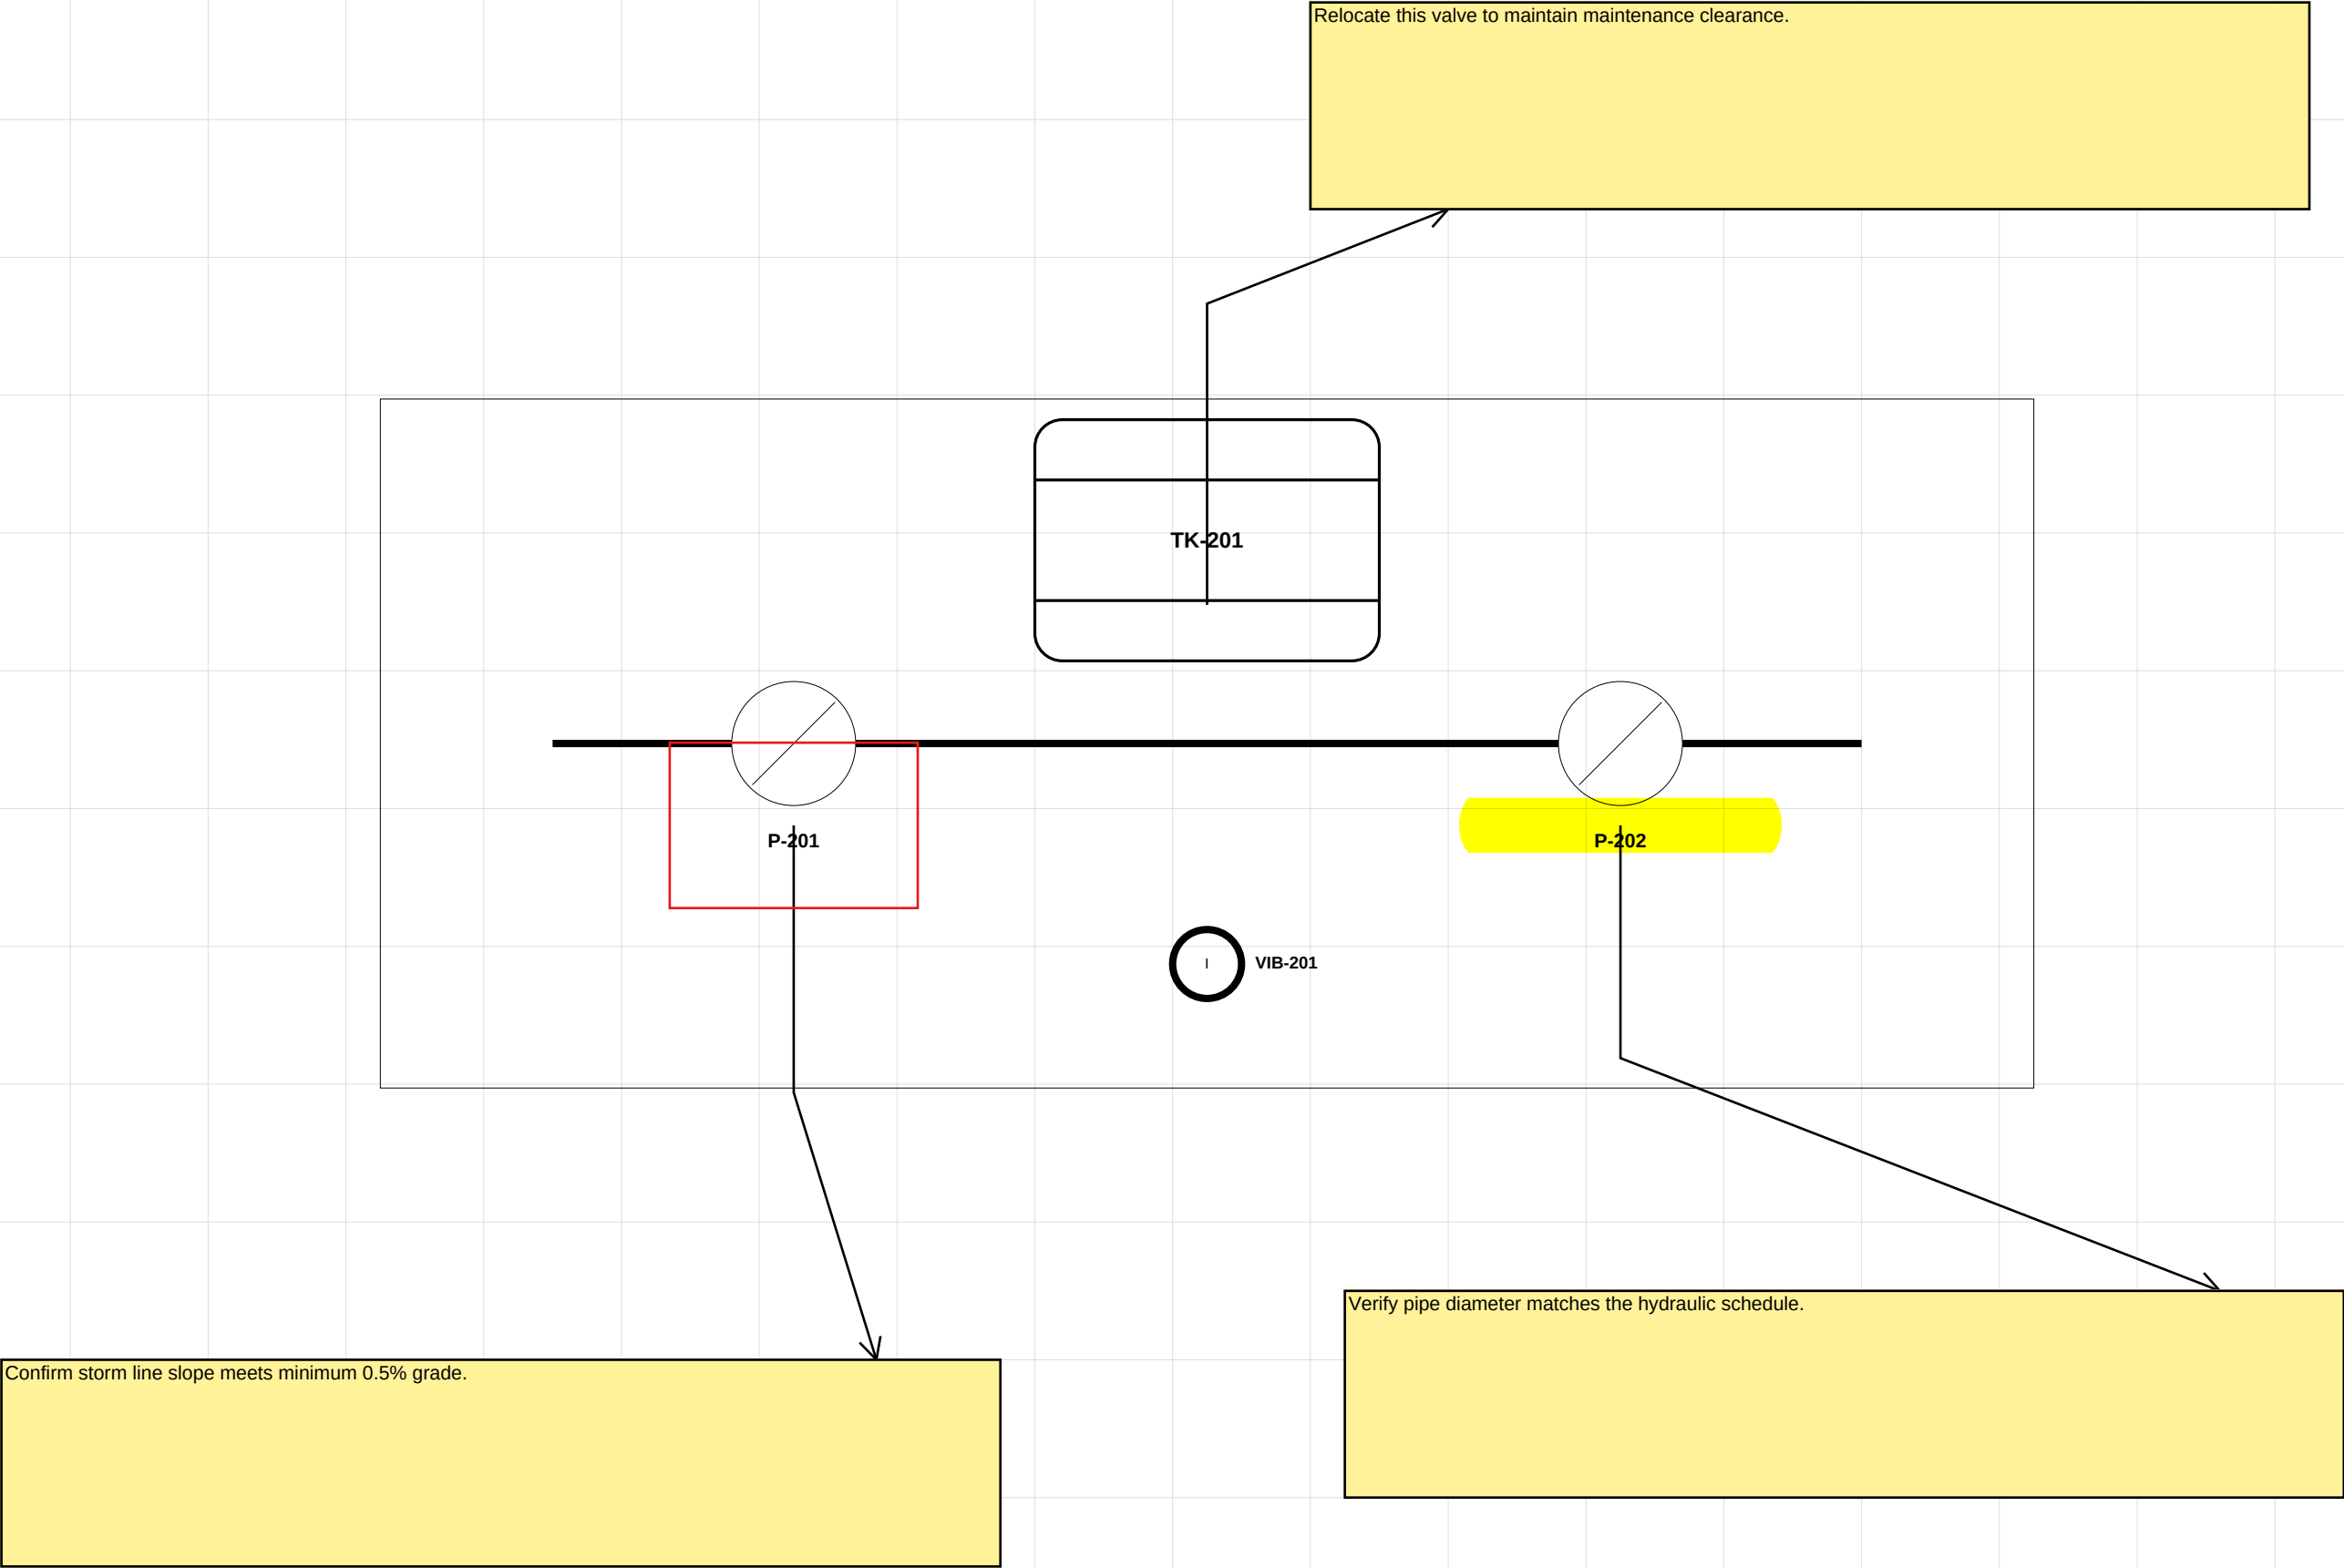

PIPING ISOMETRIC

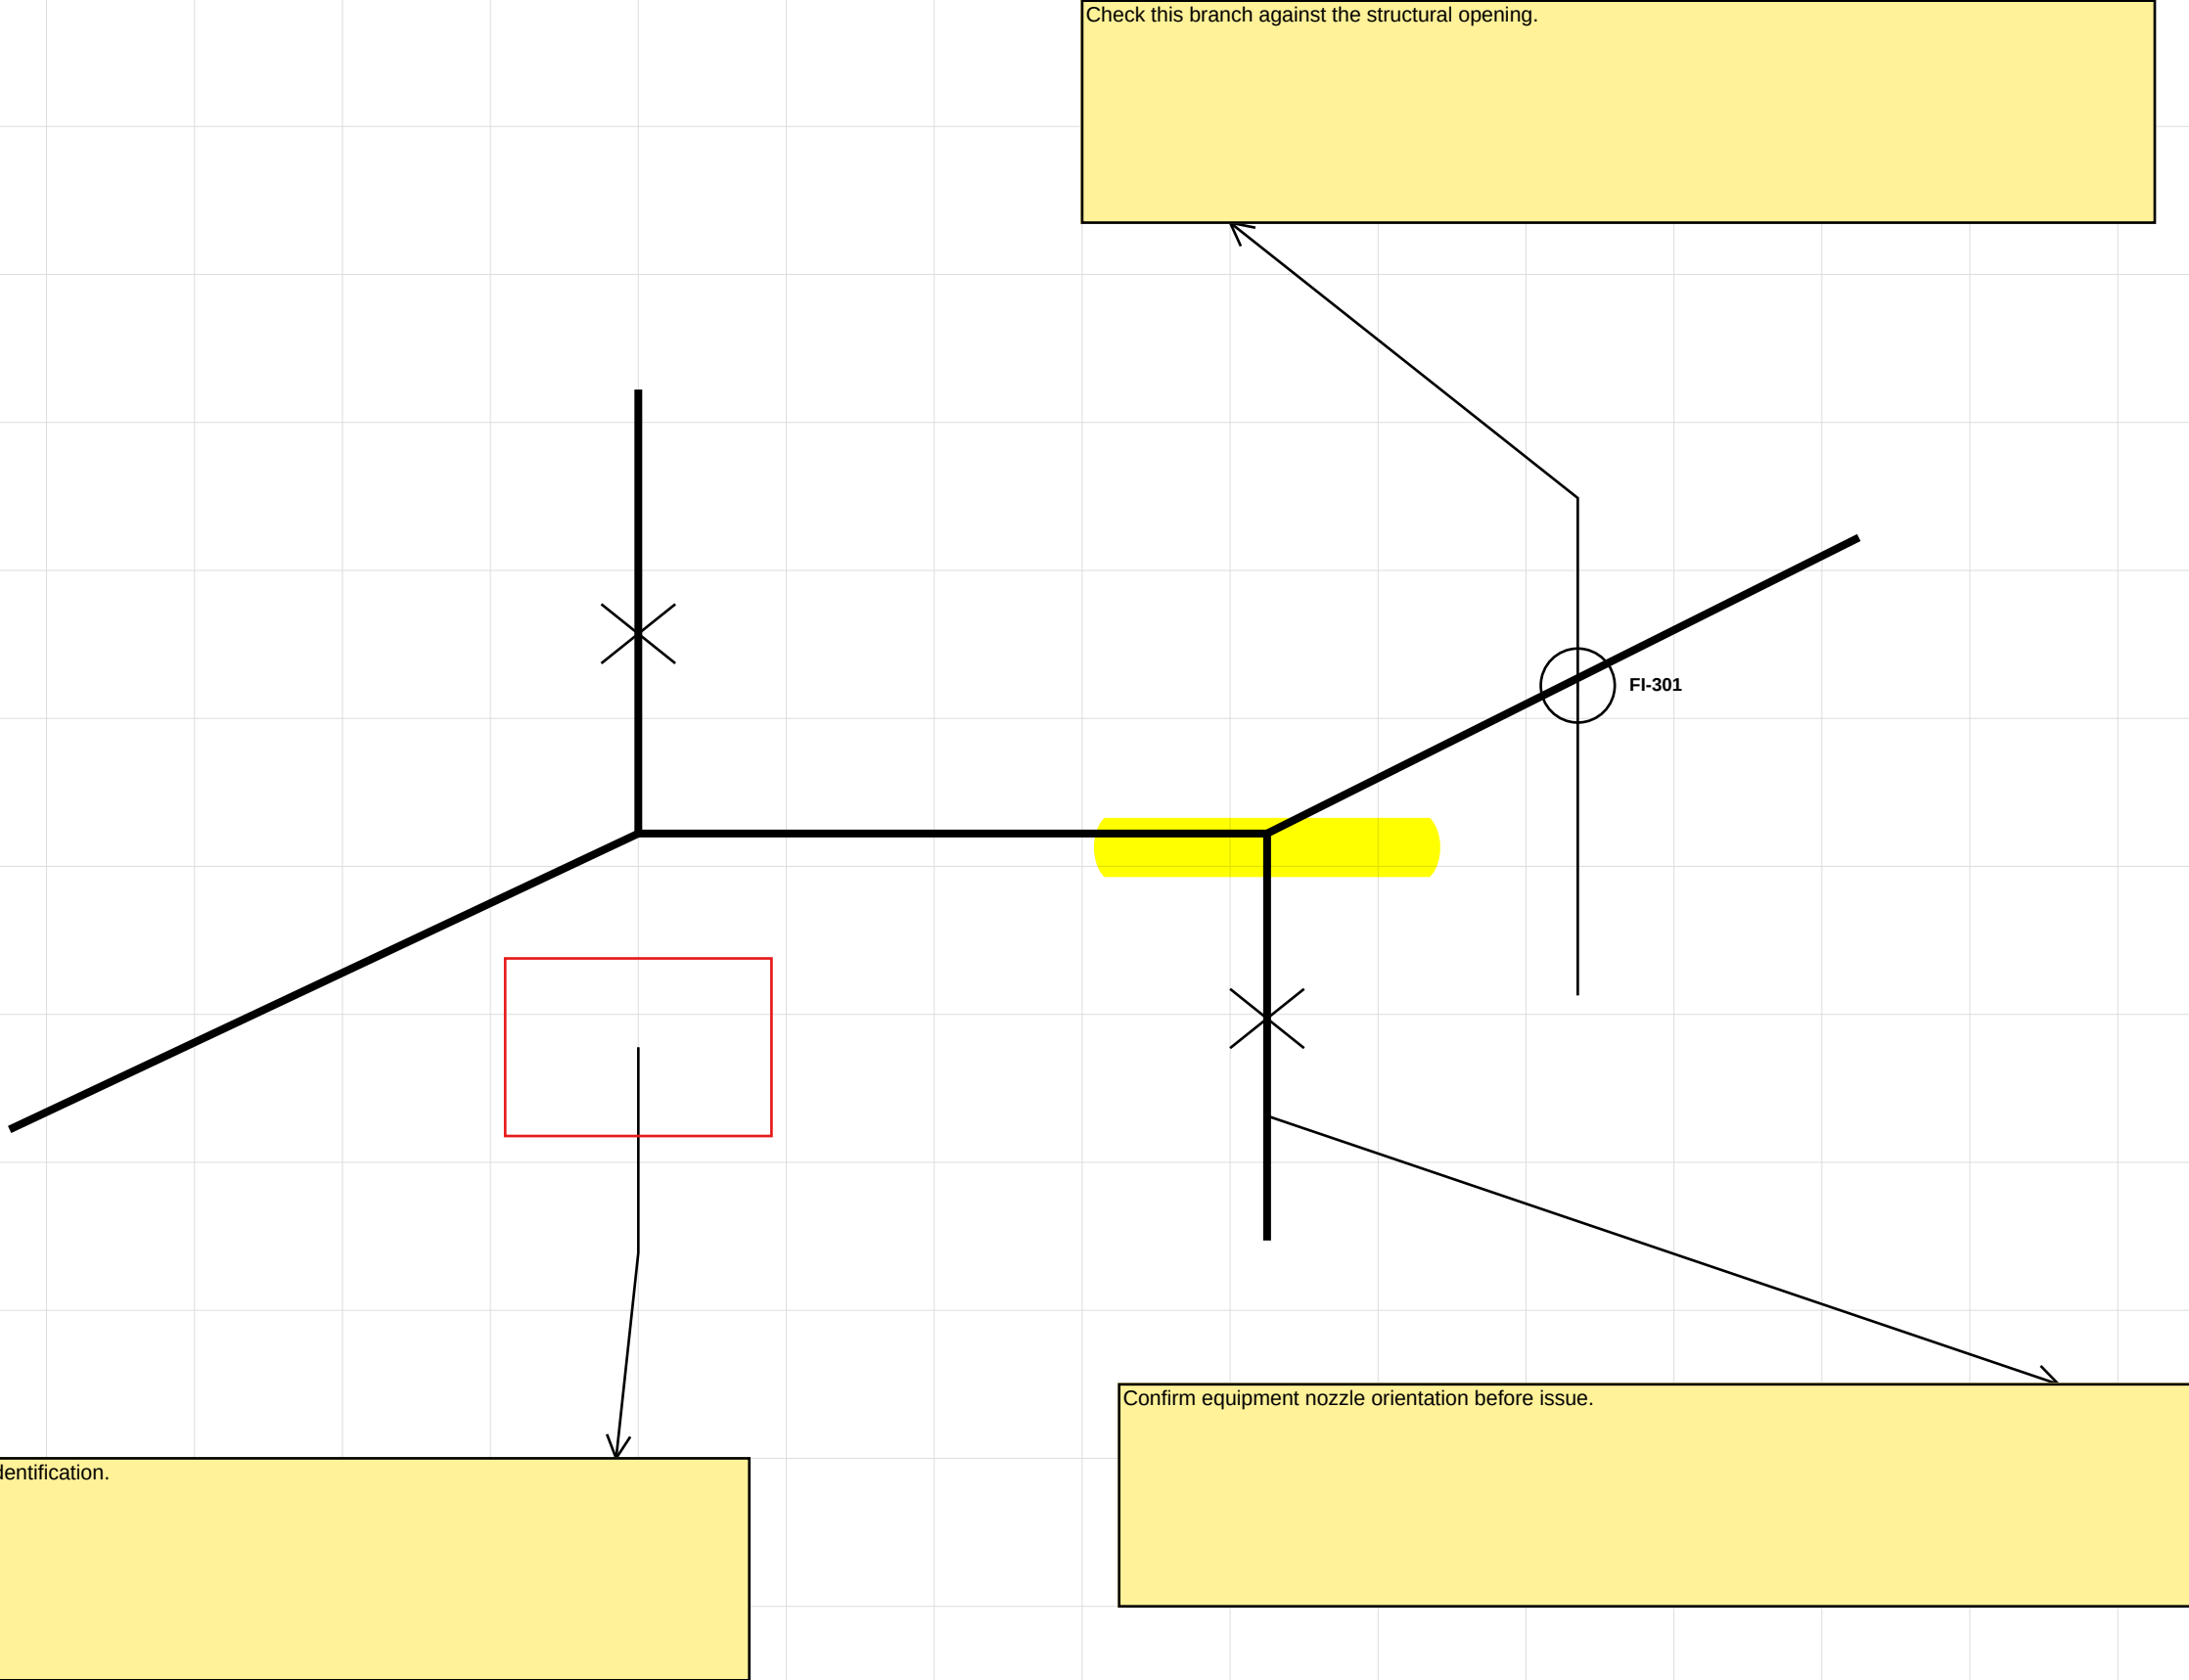


PROCESS FLOW DIAGRAM

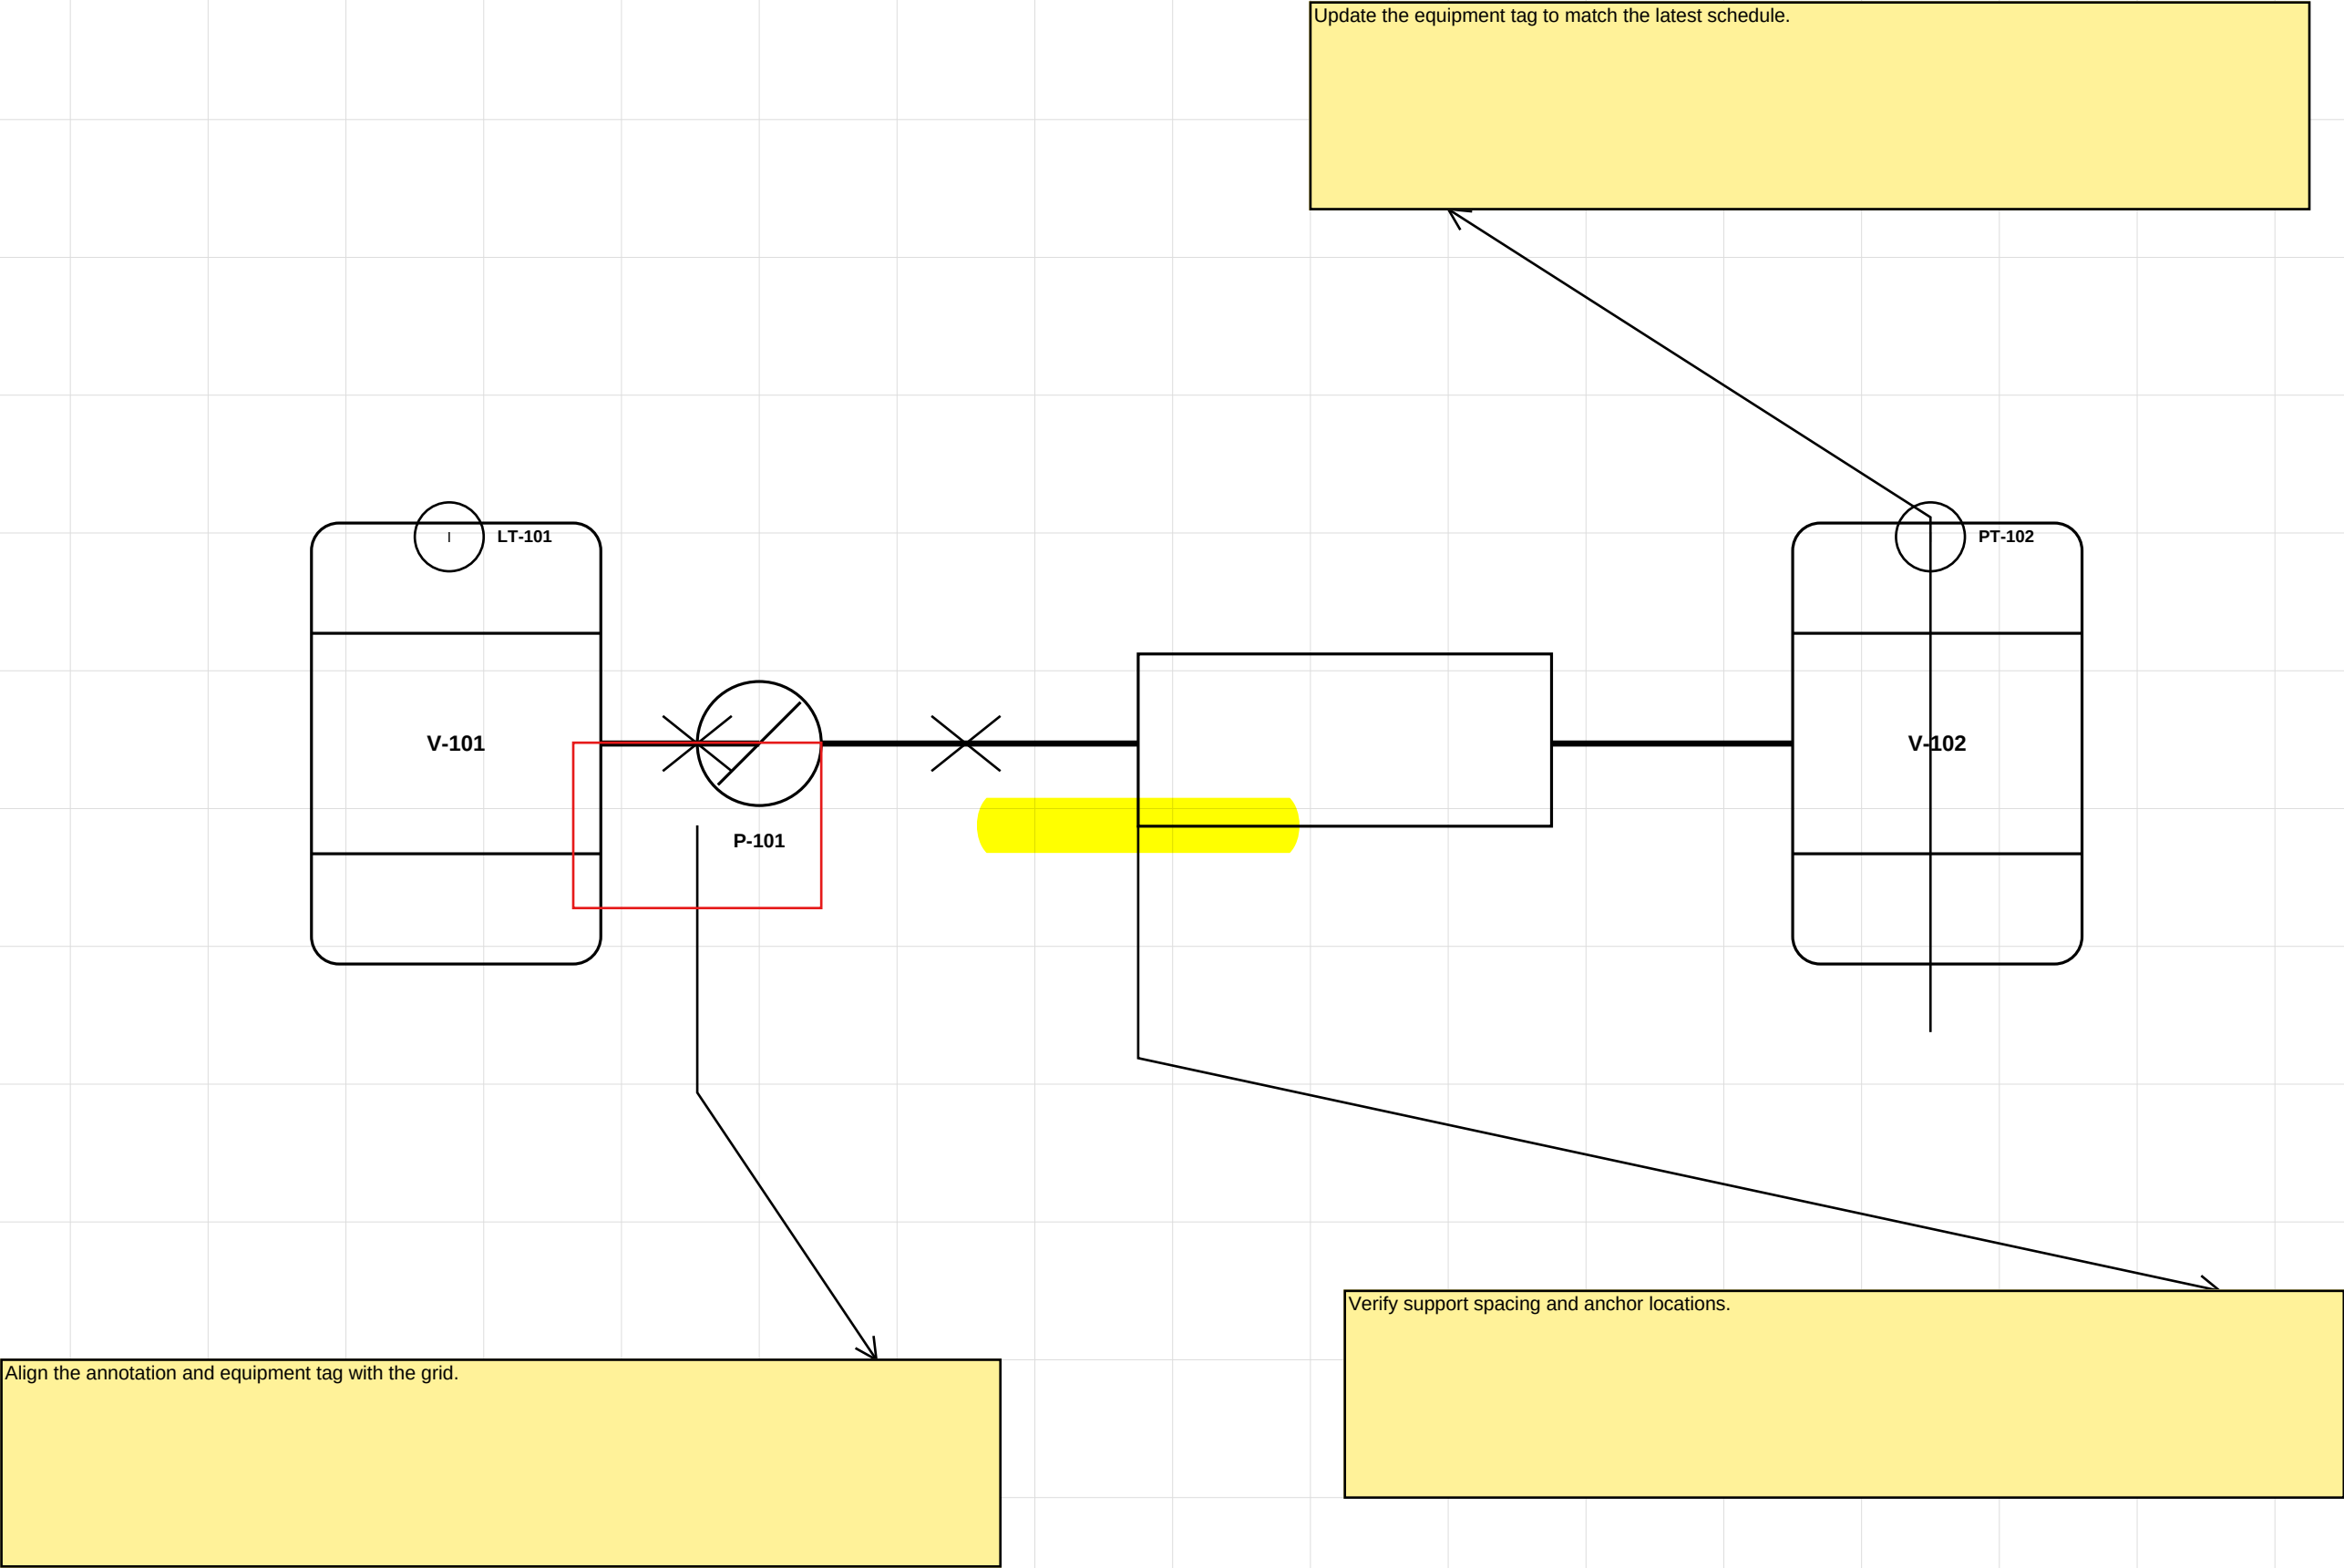



PIPING & INSTRUMENTATION LAYOUT

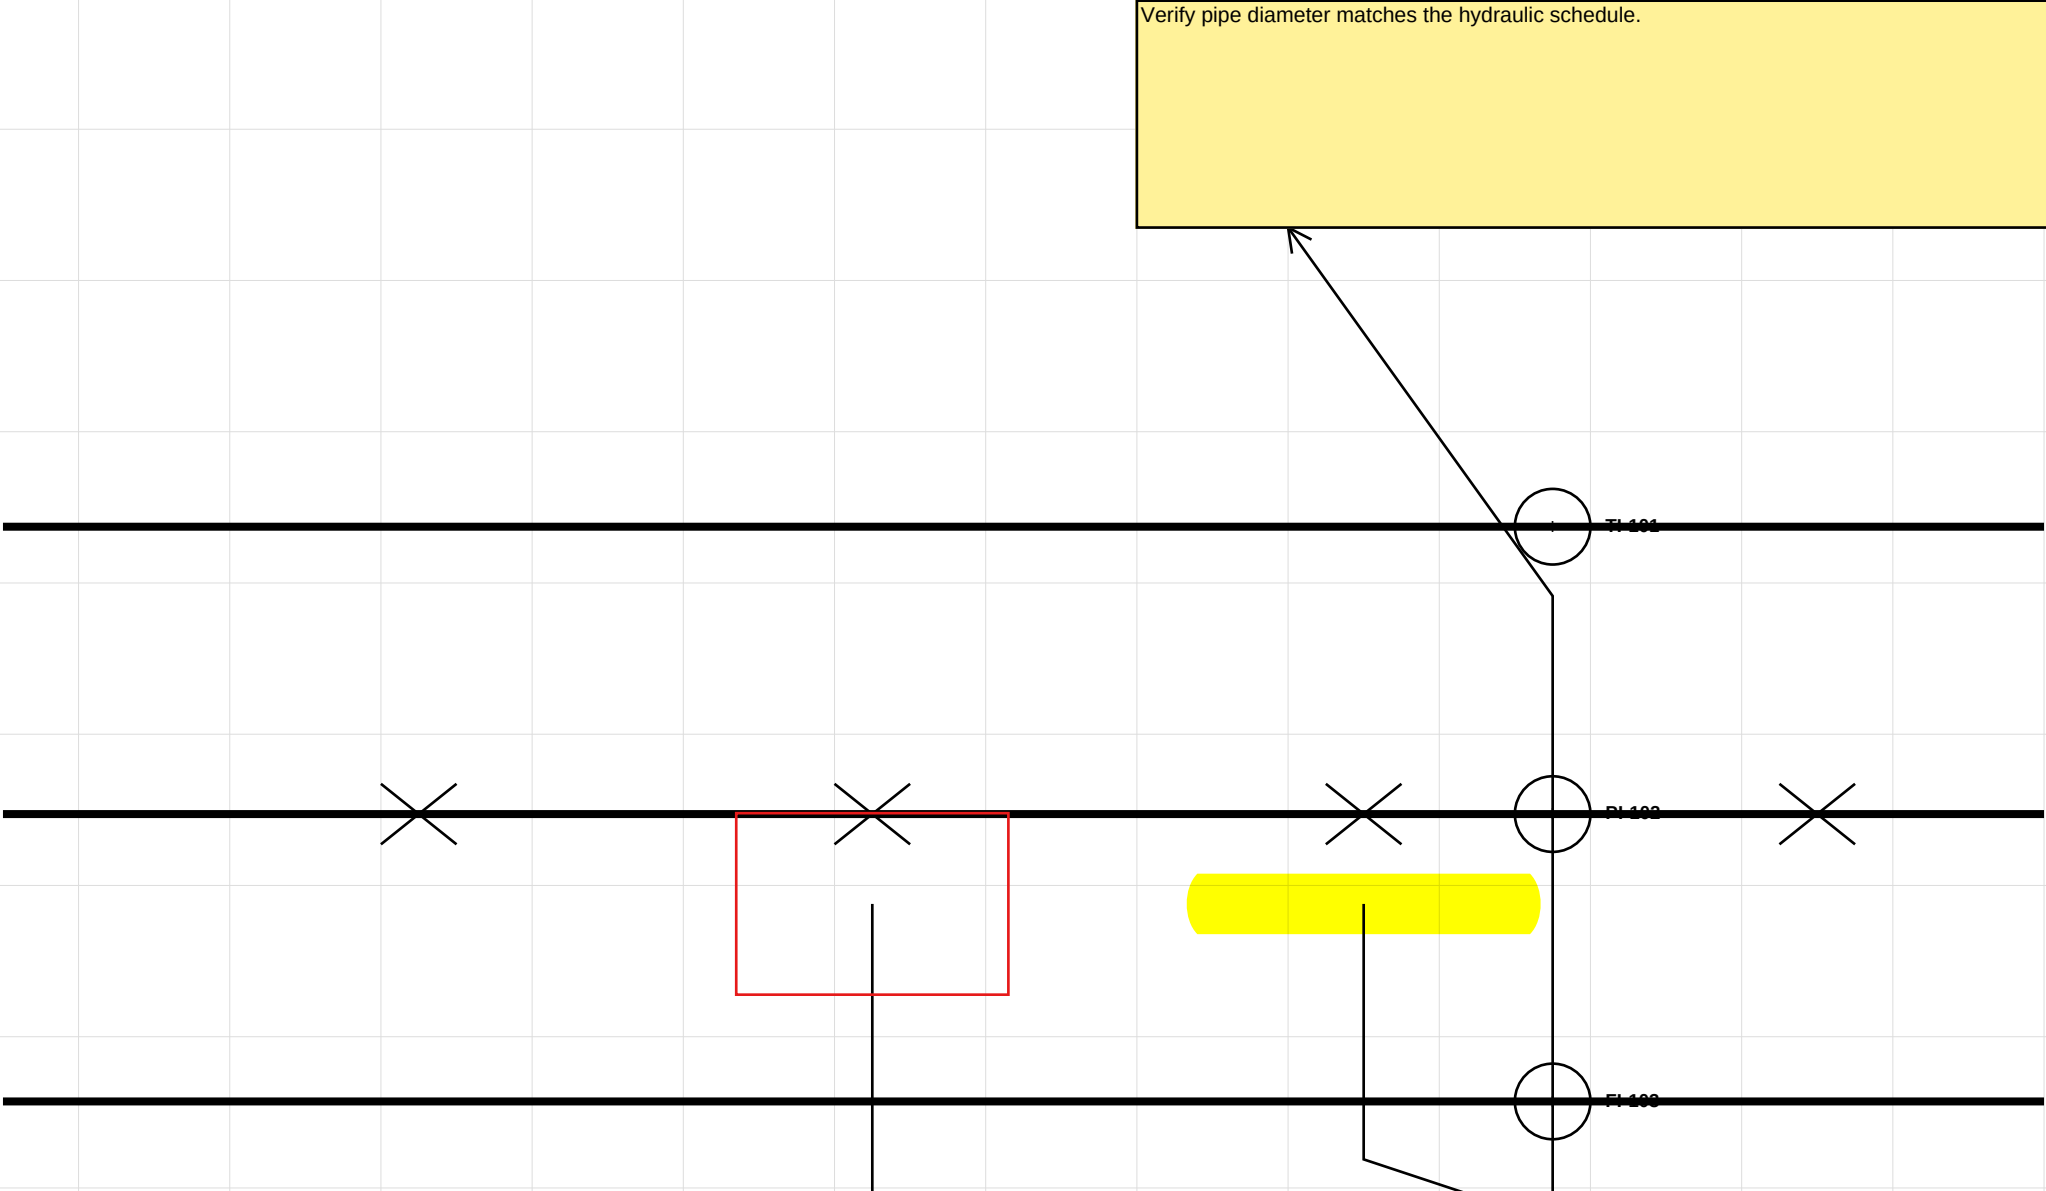


Verify pipe diameter matches the hydraulic schedule.

Confirm access clearance around the pump skid.


Confirm storm line slope meets minimum 0.5% grade.

GENERAL PLANT LAYOUT

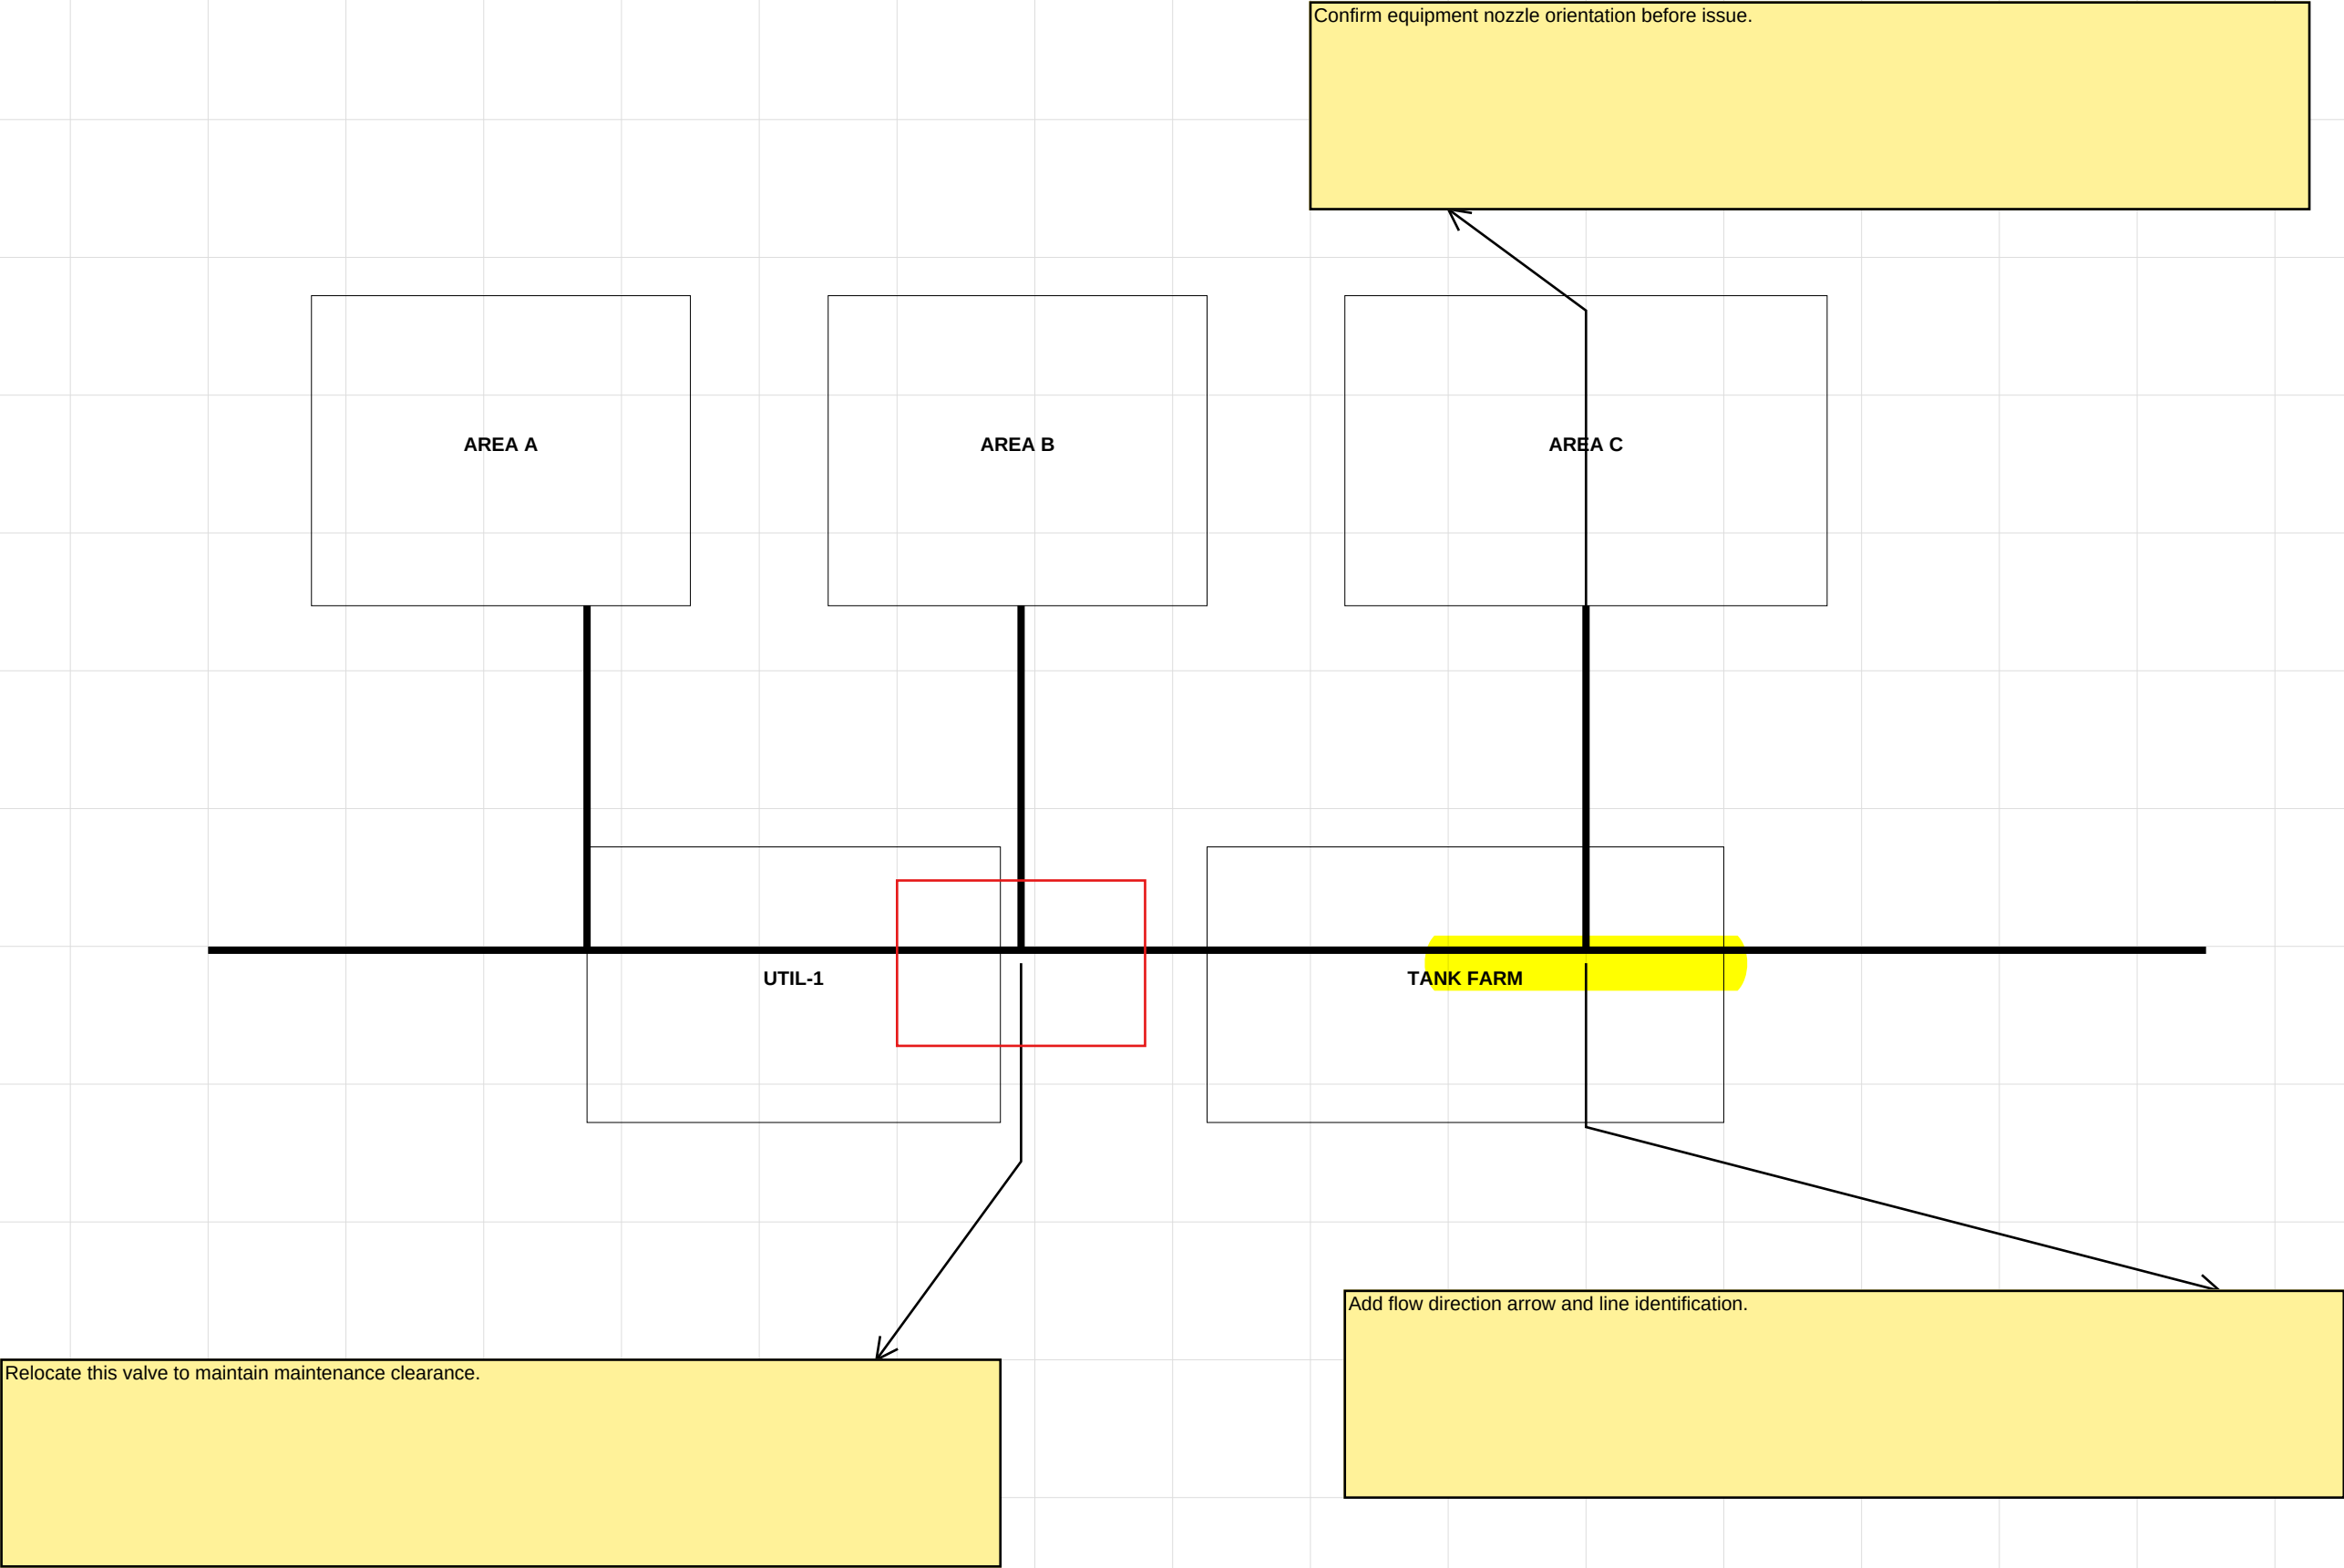



EQUIPMENT ARRANGEMENT

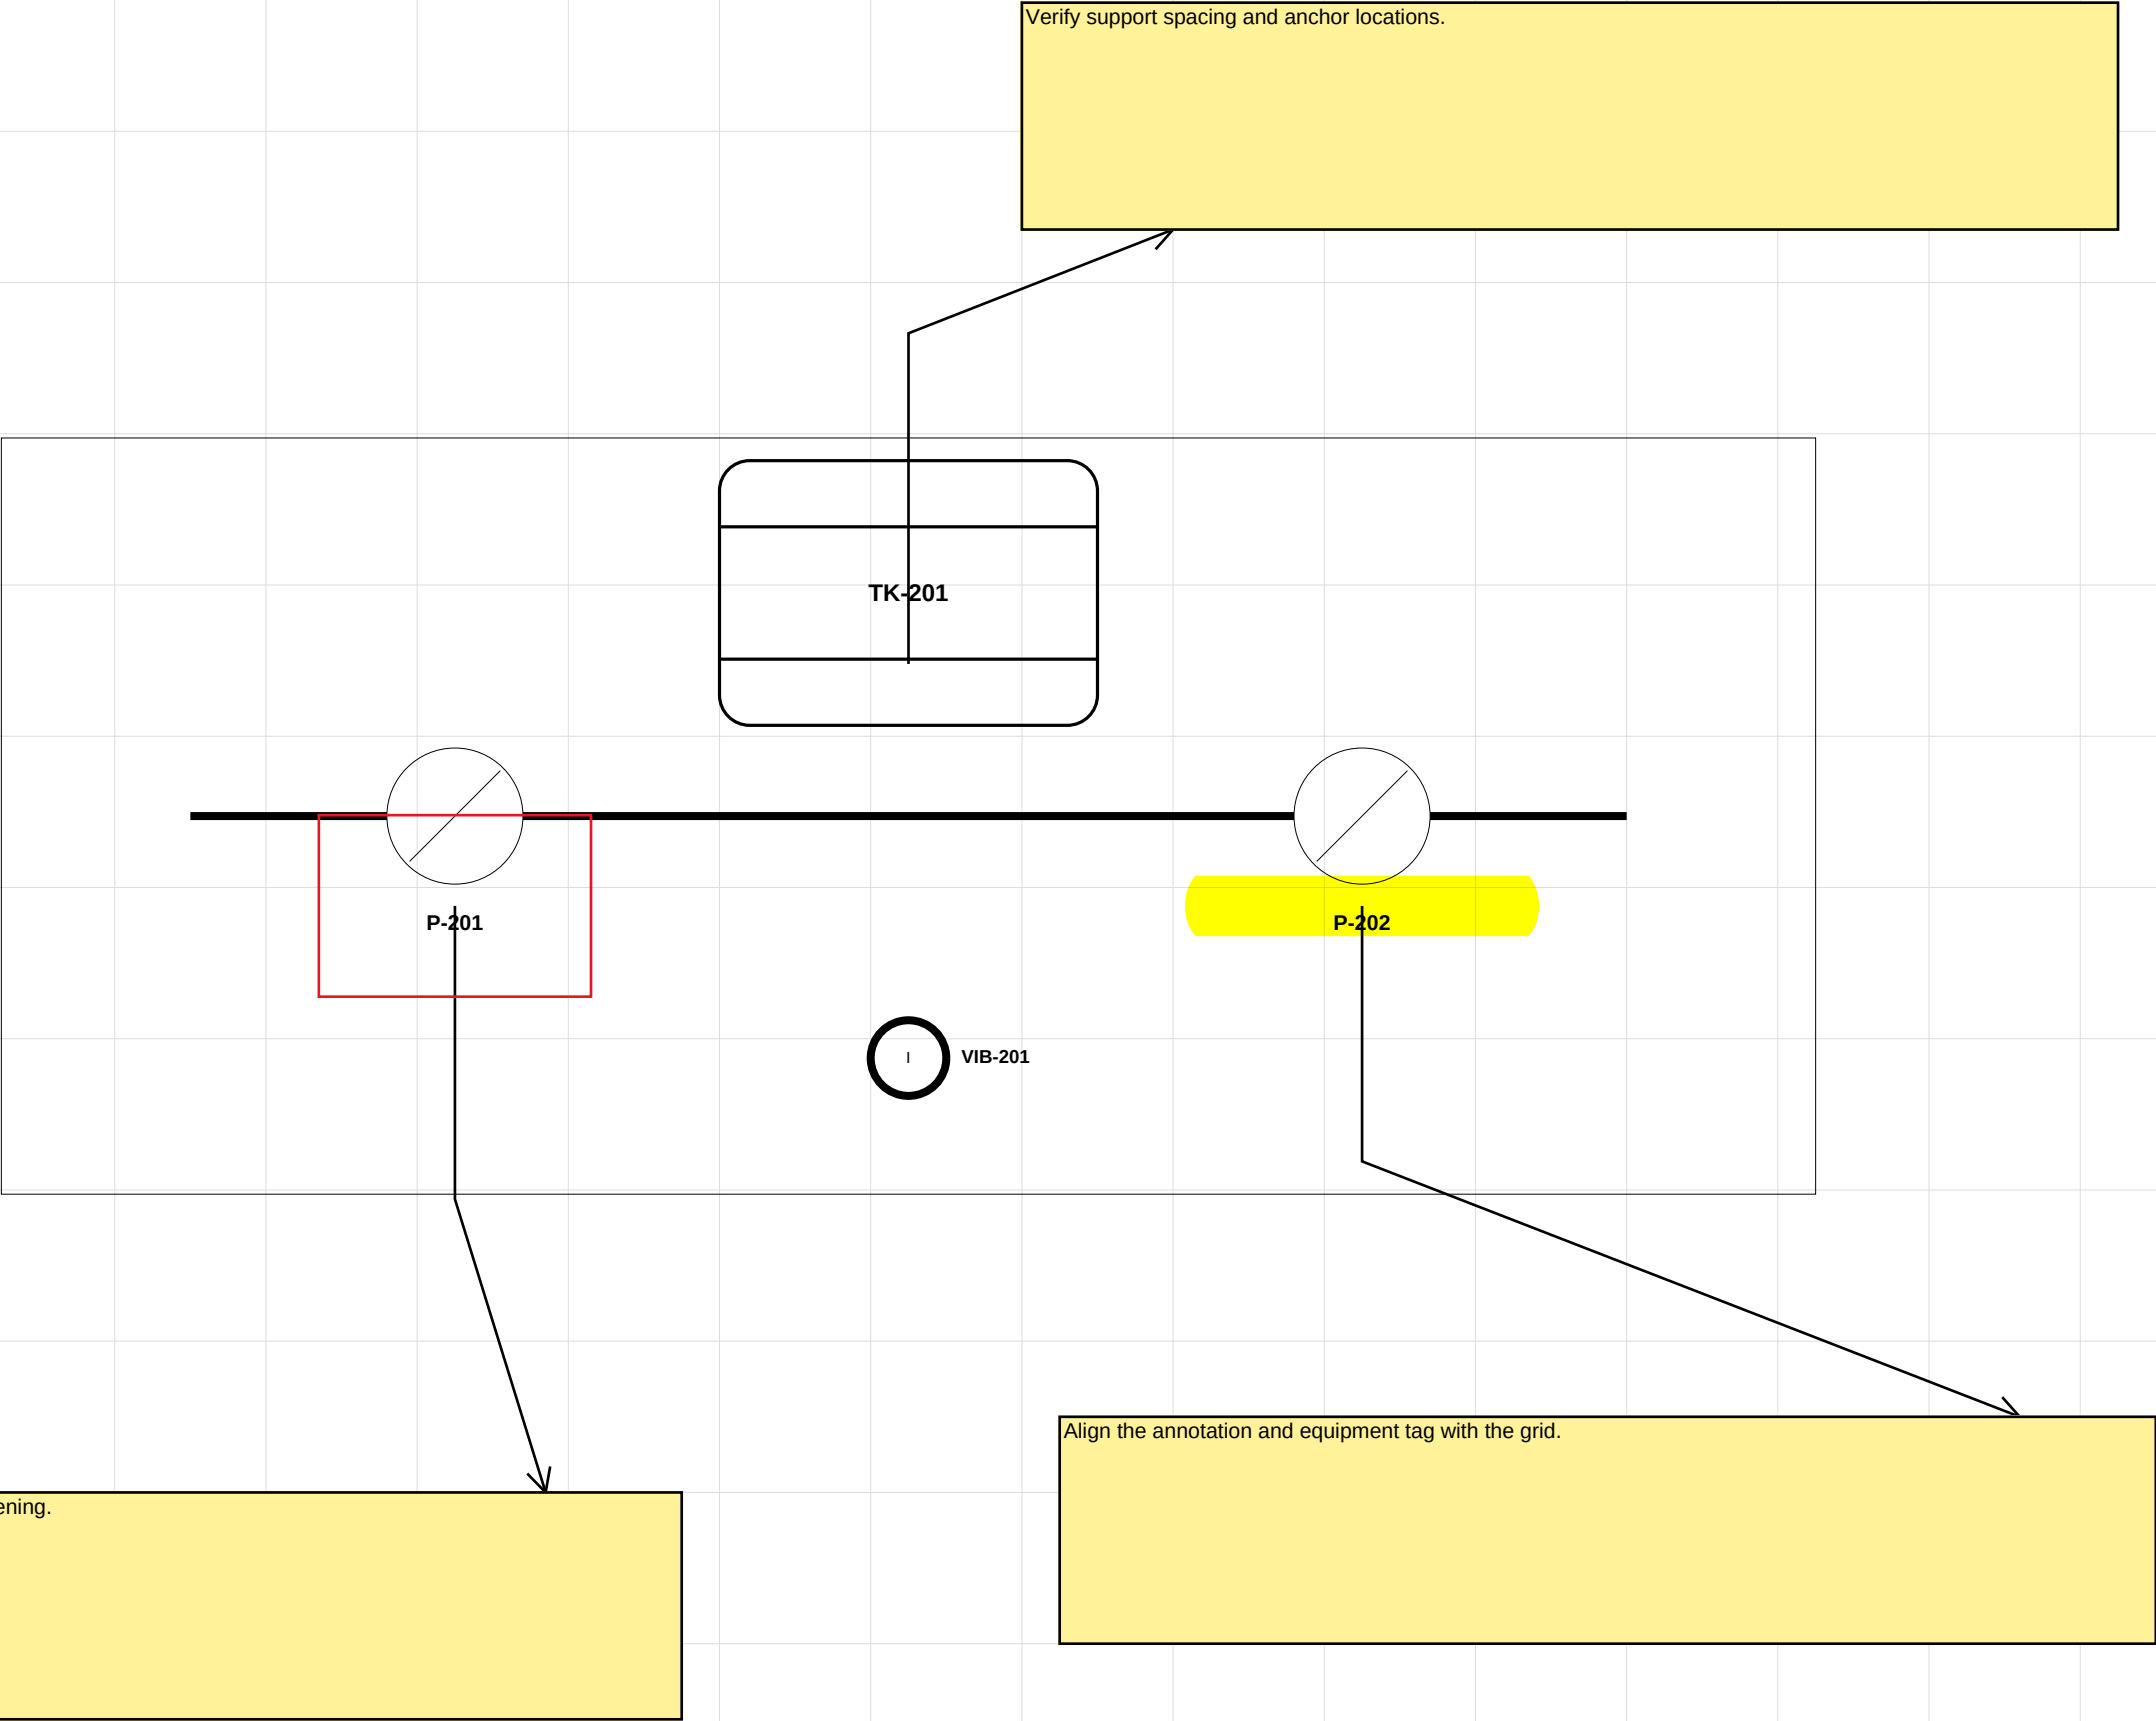

PIPING ISOMETRIC

